



Numri i Protokollit

190/2020

Republika e Kosovës
Republika Kosova-Republic of Kosova
Qeveria -Vlada-Government

Ministria e Mjedisit dhe Planifikimit Hapësinor /Ministarstvo Sredine i Prostornog Planiranja/Ministry of Environment and Spatial Planning

AGJENCIA KADASTRALE E KOSOVËS/ KATASTARSKA AGECAJA KOSOVA/ KOSOVA CADASTRAL AGENCYFormulari nr. 5**KËRKESË PËR SHERBIMET KADASTRALE NGA GJEODETI APO KOMPANIA GJEODETE E LICENCUAR**

Gjeodeti / Kompania gjeodete e licencuar: Liridon Sejdiu	Numri i licencës: 140
--	-----------------------

Komuna: Ferizaj	Zona Kadsatrale: Bibaj
-----------------	------------------------

Numri i njësisë kadastrale: 598-28

1. Të dhënat për parashtruesin e kërkesës

Emri / Emri i Kompanisë: Mexhid	Mbiemri: Behluli	Emri i prindit: Hafiz
---------------------------------	------------------	-----------------------

Numri personal: 1011785421	Adresa: Fsh. Bibaj- Ferizaj
Numri i biznesit: (për person juridik dhe kompani)	Nr. Tel: 044-935-934

2. Parashtruesi i kërkesës: Pronar - Shfrytëzues - Përfaqësues i Autorizuar**3. Lista e dokumenteve të nevojshme:**

Pronari/Shfrytëzuesi	Përfaqësues i Autorizuar
1 <input checked="" type="checkbox"/> Letërnjoftimin / Certifikatë biznesi (kopje)	1 <input type="checkbox"/> Letërnjoftimin / Certifikatë biznesi (kopje)
2 <input checked="" type="checkbox"/> Vërtetimi i tatimit në pronë	2 <input type="checkbox"/> Vërtetimi i tatimit në pronë
3 <input type="checkbox"/> Çertifikata e pronës	3 <input type="checkbox"/> Çertifikata e pronës
4 <input type="checkbox"/> Kopja e planit	4 <input type="checkbox"/> Kopja e planit

4. Kërkesa për:

1 <input checked="" type="checkbox"/> Ndërrim të kulturës së parcelës	6 <input type="checkbox"/> Matjen dhe regjistrimin e ndërtesës
2 <input type="checkbox"/> Ndarjen e parcelës	7 <input type="checkbox"/> Matjen dhe regjistrimin e pjesës së ndërtesës
3 <input type="checkbox"/> Bashkimin e parcelës	8 <input type="checkbox"/> Punë të veçanta gjeodezike
4 <input type="checkbox"/> Përcaktimin e kufijve të parcelës	9 <input type="checkbox"/> Matja e ndërtesës për legalizim
5 <input type="checkbox"/> Ri-rregullimin e kufirit të parcelës	10 <input type="checkbox"/> Riregjistrim i pjesës grafike



Nënshkrimi:

Data:

21.08.2020



Matje Gjeodezike
Shërbime Kadastrale
Projektime Inxhinerike
Tel: +383 (0) 49-535-250
liridonsejdiu88@gmail.com

N.SH. "Geo Coding"

Faturë

Nr: 22/2020

Shitësi:

N.SH. "Goe Coding"

Pronari: LIRIDON SEJDIU
NRB: 811384528
Numri Fiskal: 811384528
Adresa: Rr. "12 Qershori" - Ferizaj
BPB - 13-04-0010027832.69
LL/Bankare 130400100278326000.00%

Blerësi:

Mexhid (Hafiz) Behluli

Nr. ID. 1011785421
NRB:
Nr. Fiskal:
Adresa:
LL/Bankare

Nr.	Përshtkrimi	Njësi matëse	Sasia	Çmimi	Vlera totale
1	Ndarje e parcelës kadastrale nr 00598-28 Z. K. Bibaj	cop	3	20.00	60.00
					-
					-
					-
					-
					-
Totali:					€ 60.00

Data: 22.08.2020

Pagesa: Cash

Komenti: 1. BPB 13-04-0010027832.69
2. Banka Ekonomike 1304001002783269

Pranoi:



Dorëzoj:



Republika e Kosovës

Republika Kosova - Republic of Kosovo

Qeveria e Kosovës - Vlada Kosova - Government of Kosovo

Ministria e Infrastrukturës dhe Ambientit/ Ministrastvo Infrastrukture i Sredine/ Ministry of Infrastructure and Environment

AGJENCIA KADASTRALE E KOSOVËS/ KOSOVSKA KATASTARSKA AGENCIJA/ KOSOVA CADASTRAL AGENCY

MBËSHTJELLËS I LËNDËS

Gjeodeti / Kompania gjeodete e licencuar: **LIRIDON SEJDIU**

Numri i licencës: **140**

Numri i Protokollit: **190/2020**

LËNDA:

1. Ndërrim të kulturës së parcelës
2. Ndarjen e parcelës
3. Bashkimin e parcelës
4. Përcaktimin e kufijve të parcelës
5. Ri-rregullimin e kufirit të parcelës
6. Matjen dhe regjistrimin e ndërtesës
7. Matjen dhe regjistrimin e pjesës së ndërtesës
8. Regjistrimi i servitutit
9. Punë të veçanta gjeodezike
10. Matja e ndërtesës për legalizim

“GJEODET I LICENCUAR”

+383 44 791 828

e-mail: liridonsejdiu88@gmail.com

Data: **24/08/2020**

Vendi: **FERIZAJ**

.....

(Nënshkrimi dhe vula)

Përbajtja:

1. Kërkesa e palës
 2. Dëshmia e burimit të të dhënave zyrtare
 3. Dëshmia e pagesës për të dhënat e pranuara
 4. Fatura apo kuponi fiskal e lëshuar shërbimet kadastrale sipas UA 11/2019 dhe 12/2019
 5. Procesverbali nga terreni
 6. Manuali i njësive kadastrale
 7. Regjistri i ndërrimeve
 8. Lista e koordinatave të matura
 9. Formulari i korrigjimit të sipërfaqes
 10. Leternjoftimi i pronarit
 11. Certifikatën e pronësisë
 12. Raporti teknik
 13. Leternjoftimi kopje i fqinjëve
 14. Dokumentacioni i gjeodetit të licencuar

Dokumente tjerar:



REPUBLIKA E KOSOVËS
РЕПУБЛИКА КОСОВО
REPUBLIC OF KOSOVO

LETENSKI LISTA - IDENTITY CARD

Mbiemri/Презиме/Name

BEHLULI

Esimu/Име/First name

MEXHIT

Gjina/Лин/Sex

M

Dita e lindjes/Датум рођене/Date of birth

20.11.1941

Vendi i lindjes/Mesto rođenja/Place of birth

UGLAR

Dita e skadimit/Датум истека/Date of expiry

Përhershëm/Trajna/Permanent



Dita e lesimit/Датум издавања/Date of issue

14.07.2009

QKRC/ОЦПР/MICRC

2501S

Leshuar nga/Сајака која издаје/Issuing authority

MPB / MUP / MIA

Numri personal/Лични број/Personal number

1011785421

Nr.lni/Бр.лк/Id no

ID02791276



044 935 939

1 : 500

Auto

Kërko në bazën tekstuale
Menya e kerkimit

Pjesa e numrit kadastral
598

Komuna
FERIZAJ

Zona kadastrale
Bibaj

Adresa

Kërkohet

**Detajet e njësisë kadastrale**

ID e njësisë
P-72217006-00598-28

Tipi i njësisë
parcel / PARCELË / PARCELA

Sipërfaqja tekstuale
5616

Sipërfaqja grafike
5615.8

Informata shtesë**Shfrytëzimi aktual****Të drejtat**

Tipi i duhur
EN: Ferizaj
SQ: Ferizaj
SR: Uroševac

Data e përfundimit
Mon Jan 01 0001 01:00:00 GMT+0100 (W. Euro...

Tipi

EN: sinç

SQ: Posedim

SR: Dzavina

EN: Ferizaj

SQ: Ferizaj

SR: Uroševac

A10:3

Personi

Emri
MEXHID

Mbiemri
BEHLULLI

Emri i babait
HAFIZ

Tipi i ID-së
KosovoIDCard / Leternjoftimi / Licna karta



Republika e Kosovës
Republika Kosova-Republic of Kosovo
Qeveria e Kosovës- Vlada Kosova- Government of Kosovo
Ministria e Infrastrukturës dhe Ambientit/ Ministrastvo Infrastrukture i Sredine/ Ministry of
Infrastructure and Environment

AGJENCIA KADASTRALE E KOSOVËS/KOSOVSKA KATASTARSKA AGENCIJA/ KOSOVO CADASTRAL AGENCY

PROCESVERBALI NGA TERRENI

Gjeodeti / Kompania gjeodete e licencuar: Liridon Sejdiu	Numri i licencës: 140
Komuna: Ferizaj	Zona Kadastrale: Bibaj
Numri i njësisë kadastrale: 00598-28	

Matja/piketimi është realizuar me:
GPS/GNSS <input checked="" type="checkbox"/>
Stacion Total <input type="checkbox"/>

1. Përshkimi i procesit:

NDARJA ËSHTË BËRË PËR TË KUSHTETZUAR NGA ANA PERENDIMORE PARC. 1 AR 15ARI, 2 NË 15ARI DHE E KUNDIT 23% m² PARC. E DITË NËK ANA PERENDIMORE LINJA E NDARIS VENDOSUR NGJËN 90° KUR SE LINJA PERENDIMORE 3.25 mëgj. linja NORTË 90°

2. Vërejtje:

3. Nënshkrimi i palëve

Pronarët janë pajtuar me pikat definitive kufitare të vendosura në terren nga të cilat derivohet sipërfaqja definitive që do të regjistrohet në Sistemin e Informacioneve Kadastrale për Tokën në Kosovë.

Të poshtëshënuarve u lexohet procesverbal i dëshmi i përmes që nëse pajtohen me atë nënshkrujnë më poshtë, në të kundërtën jepin arsyet e mospajtimit.

Emri (emri i prindit) mbiemri	Numri personal	Numri i njësisë kadastrale	Nënshkrimi
QENDRIJA BELLILI	1233200388	00598-28	<i>Ling Mary Thomas</i>
FATMIRE HERZ	1091800170		<i>Fatmire Herz</i>
THOMAS MARY	946168010891512239		

Nënshkrimi dhe vula e gjeodetit:



Data: 21.08.2020

Gjeodeti i licencuar: LIRIDON SEJDIU Numri i licencës: 140

Adresa: Rr. "12 Qershori" pn Ferizaj



Republika e Kosovës
Republika Kosova-Republic of Kosova
Qeveria - Vlada-Government
Ministria e Mjedisit dhe Planifikimit Hapësinor /Ministarstvo Sredine i Prostornog Planiranja/Ministry of Environment and Spatial Planning
AGJENCIJA KADASTRALE E KOSOVËS/ KATASTARSKA AGECIJA KOSOVA/ KOSOVA CADASTRAL AGENCY

Zyra kadastrale komunale / Opštinska katastarska kancelarija: Ferizaj


Nr. i njësisë kadastrale / Br. katastarske jedinice : 598-28

Zona kadastrale / Katastarska zona: Bibaj

Numri i lëndës / Broj predmeta: _____

Lloji i njësisë kadastrale / Vrsta katastarske jedinice : Parcel

Shkalla e zvoglimit / Razmerra plana : 1:1000

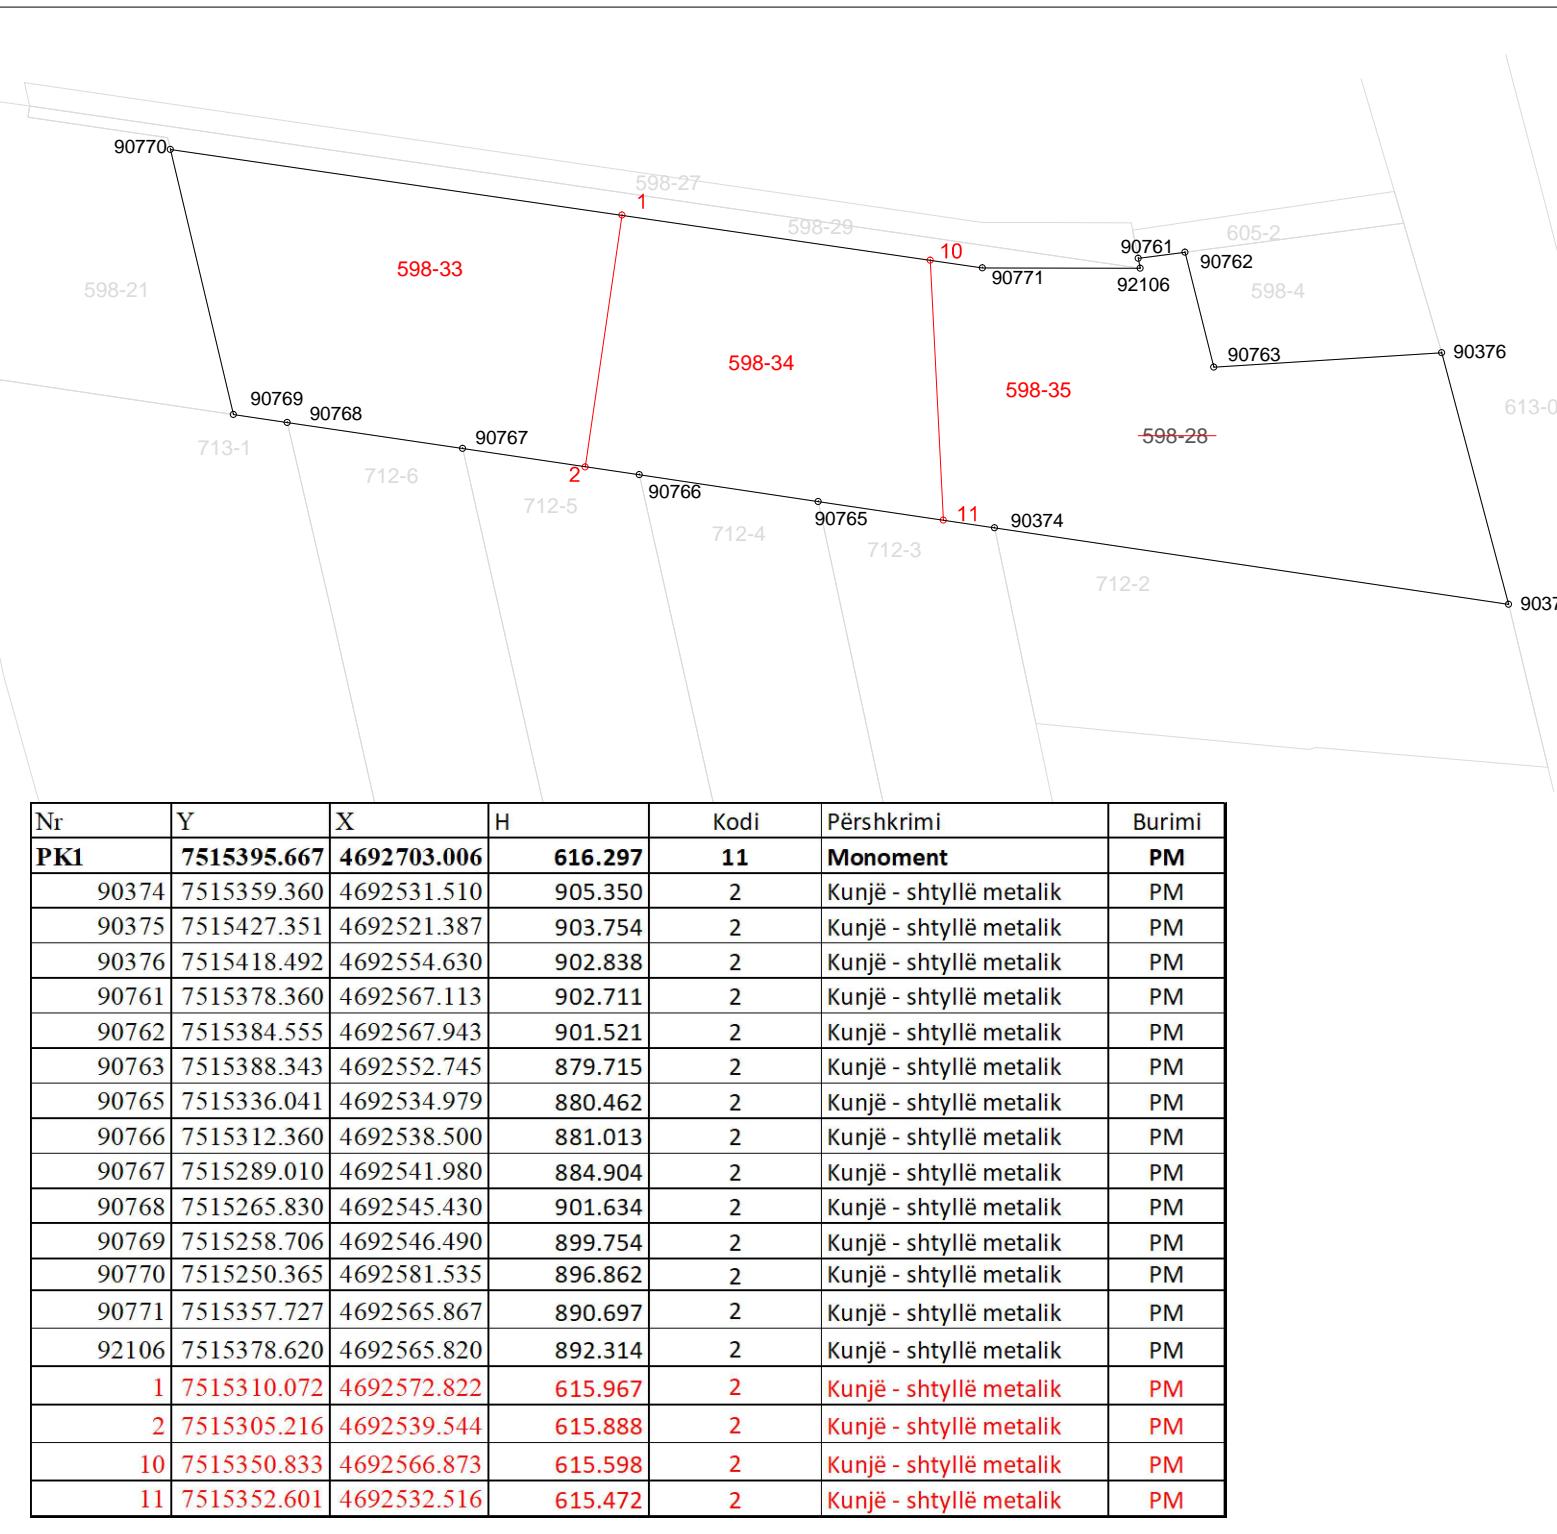

Nr	Y	X	H	Kodi	Përshtkimi	Burimi
PK1	7515395.667	4692703.006	616.297	11	Monoment	PM
90374	7515359.360	4692531.510	905.350	2	Kunjë - shtyllë metalik	PM
90375	7515427.351	4692521.387	903.754	2	Kunjë - shtyllë metalik	PM
90376	7515418.492	4692554.630	902.838	2	Kunjë - shtyllë metalik	PM
90761	7515378.360	4692567.113	902.711	2	Kunjë - shtyllë metalik	PM
90762	7515384.555	4692567.943	901.521	2	Kunjë - shtyllë metalik	PM
90763	7515388.343	4692552.745	879.715	2	Kunjë - shtyllë metalik	PM
90765	7515336.041	4692534.979	880.462	2	Kunjë - shtyllë metalik	PM
90766	7515312.360	4692538.500	881.013	2	Kunjë - shtyllë metalik	PM
90767	7515289.010	4692541.980	884.904	2	Kunjë - shtyllë metalik	PM
90768	7515265.830	4692545.430	901.634	2	Kunjë - shtyllë metalik	PM
90769	7515258.706	4692546.490	899.754	2	Kunjë - shtyllë metalik	PM
90770	7515250.365	4692581.535	896.862	2	Kunjë - shtyllë metalik	PM
90771	7515357.727	4692565.867	890.697	2	Kunjë - shtyllë metalik	PM
92106	7515378.620	4692565.820	892.314	2	Kunjë - shtyllë metalik	PM
1	7515310.072	4692572.822	615.967	2	Kunjë - shtyllë metalik	PM
2	7515305.216	4692539.544	615.888	2	Kunjë - shtyllë metalik	PM
10	7515350.833	4692566.873	615.598	2	Kunjë - shtyllë metalik	PM
11	7515352.601	4692532.516	615.472	2	Kunjë - shtyllë metalik	PM

Rilevoi / Snimio: LIRIDON SEJDIU
(emri dhe mbiemri i gjeodetit/kompanisë/ ime i prezime geodeta/ kompanije)

Nr. i licencës / Br. licence: 140

Aprovoi / Usvojio: _____
(emri dhe mbiemri i pësonit zyrtar/ ime i prezime sluzbenog lica)

Nënshkrimi / Potpis: _____

V.V.

Nënshkrimi / Potpis: _____

Data e rilevimit / Datum snimanja: 21.08.2020

Data e aprovimit / Datum usvajanja: _____



Point Id	/	Point Class	Date/Time	Easting	Northing	Ellip. Hgt.	Posn. + Hgt. Qlty
<input checked="" type="checkbox"/> A1		Measured	08/21/2020 16:30:23	7515310.0625	4692572.8075	615.9668	0.0334
<input checked="" type="checkbox"/> A2		Measured	08/21/2020 16:32:01	7515305.2302	4692539.5411	615.8881	0.0141
<input checked="" type="checkbox"/> A3		Measured	08/21/2020 16:23:49	7515349.2576	4692532.9872	615.4627	0.0189
<input checked="" type="checkbox"/> A4		Measured	08/21/2020 16:22:09	7515354.1510	4692566.4092	615.5062	0.0441
<input checked="" type="checkbox"/> A5		Measured	08/21/2020 16:00:19	7515303.4536	4692573.7757	616.1362	0.0206
<input checked="" type="checkbox"/> A6		Measured	08/21/2020 16:02:06	7515311.8617	4692538.5777	615.8376	0.0182
<input checked="" type="checkbox"/> A7		Measured	08/21/2020 15:53:54	7515355.9158	4692532.0253	615.3696	0.0180
<input checked="" type="checkbox"/> A8		Measured	08/21/2020 15:52:28	7515347.5170	4692567.3560	615.5578	0.0196
<input checked="" type="checkbox"/> A10		Measured	08/22/2020 07:36:07	7515350.8503	4692566.8869	615.5976	0.0149
<input checked="" type="checkbox"/> A11		Measured	08/22/2020 07:37:37	7515352.5899	4692532.5139	615.4724	0.0171
<input checked="" type="checkbox"/> A100		Measured	08/21/2020 17:01:57	7515350.4963	4692566.9013	615.6125	0.0215
<input checked="" type="checkbox"/> A101		Measured	08/21/2020 17:05:17	7515352.3151	4692532.5464	615.4982	0.0209
<input checked="" type="checkbox"/> A736182		Measured	08/21/2020 16:08:02	7515258.6792	4692546.5257	616.4223	0.0204
<input checked="" type="checkbox"/> A736183		Measured	08/21/2020 16:06:24	7515250.3754	4692581.5406	616.6484	0.0214
<input checked="" type="checkbox"/> B1		Measured	08/21/2020 17:09:27	7515310.0680	4692572.8351	616.0586	0.0204
<input checked="" type="checkbox"/> B2		Measured	08/21/2020 17:07:38	7515305.2141	4692539.5362	615.9216	0.0190
<input checked="" type="checkbox"/> PK1		Measured	08/21/2020 18:01:31	7515395.6669	4692703.0061	616.2969	0.0246
<input checked="" type="checkbox"/> RTCM-Ref 0003		Reference	08/21/2020 17:07:39	7503168.9298	4699391.6087	628.0260	0.0000
<input checked="" type="checkbox"/> RTCM-Ref 0016		Reference	08/22/2020 07:33:56	7515330.3419	4692568.3749	615.6509	0.0000
<input checked="" type="checkbox"/> RTCM-Ref 0204		Reference	01/06/1980 01:00:00	7515326.8820	4692565.8277	613.8059	0.0000
<input checked="" type="checkbox"/> RTCM-Ref 0213		Reference	08/21/2020 17:01:27	7515350.8679	4692568.7707	612.9270	0.0000
<input checked="" type="checkbox"/> RTCM-Ref 0234		Estimated	08/21/2020 17:59:25	7515392.6787	4692699.9090	612.5949	0.0000
<input checked="" type="checkbox"/> RTCM-Ref 0235		Reference	08/21/2020 17:59:25	7515396.6661	4692705.0172	616.1408	0.0000



Republika e Kosovës

Republika Kosova - Republic of Kosovo

Qeveria e Kosovës - Vlada Kosova - Government of Kosovo

Ministria e Infrastrukturës dhe Ambientit/ Ministrastvo Infrastrukture i Sredine/ Ministry of Infrastructure and Environment
AGJENCIA KADASTRALE E KOSOVËS/ KOSOVSKA KATASTARSKA AGENCIJA/ KOSOVA CADASTRAL AGENCY

GJENDJA E VJETËR / STARO STANJE												GJENDJA E RE / NOVO STANJE																				
Numri rendor, Redni broj	Komuna	Opština	Zona kadastrale Katastarska zona	Mbiemri, Emri (Emri i Babës) Adresa e vendbanimit Prezime, Ime (Ime Oca) Adresa prebivališta 1. Pronar - Vlasnik - Owner 2. Posedues - Posednik - Possessor 3. Shfrytëzues - Korisnik - User	Nr. personal nga: Personalni Br. iz:	Nr. i Njësisë Br. Jedinice	1. (P) Parcela u/r 2. (O) Ndërtesa u/r Zgrada 3. (O) Pj. e ndërt. u/r Deo Zgrade	Kultura, klasa Shfrytëzimi aktual	Aktuelna upotreba	Sipërfaqja, Površina (m²)	Përshkrimi i gjendjes së Njësisë Opis stanja Jedinice 1. Adresa, Vend i quajtur Adresa, Zvano mesto 2. Infrastruktura Infrastruktura 3.Tjera karakterist.(referen ca) Ostale karakterist.(referen sa)	Mbiemri, Emri (Emri i Babës) Adresa e vendbanimit Prezime, Ime (Ime Oca) Adresa prebivališta 1. Pronar - Vlasnik 2. Posedues - Posednik 3. Shfrytëzues - Korisnik	Nr. i Njësisë Br. Jedinice	1. (P) Parcela u/r 2. (O) Ndërtesa u/r Zgrada 3. (O) Pj. e ndërt. u/r Deo Zgrade	Kultura, klasa Shfrytëzimi aktual	Aktuelna upotreba	Sipërfaqja, Površina (m²)	Dokumenti në të cilin bazohet ndërrimi dhe rezultati i shqimit në vend të ngjarjes nga personi zyrtar përmirëmbajtjen e kadastrit.														
												1	2	3	4	5	6	7	8	9	10	11	12	13	14							
1	Ferizaj	Bibaj	1	Mexhid (Hafiz) Behluli	1	1011785421	1	00598-28	R	Arë(3)	5616	Fusha	1	Mexhid (Hafiz) Behluli		1	00598-33	R	Arë(3)	1800	1	00598-34	R	Arë(3)	1500	1	00598-35	R	Arë(3)	2316	Gjithësej	5616
Gjeodeti/kompania e licencuar: LIRIDON SEJDIU												Nr i licencës: 140						Nënshkrimi dhe vula:														



Republika e Kosovës
Republika Kosova-Republic of Kosovo
Qeveria e Kosovës- Vlada Kosova- Government of Kosovo
Ministria e Infrastrukturës dhe Ambientit/ Ministrastvo Infrastrukture i Sredine/ Ministry of Infrastructure and Environment
AGJENCIA KADASTRALE E KOSOVËS/KOSOVSKA KATASTARSKA AGENCIJA/ KOSOVO CADASTRAL AGENCY

Komuna: Ferizaj	Zona Kadastrale: Bibaj
Numri i njësis kadastrale: 598-28	Sistemi koordinat: KosovaRef01

Nr	Y	X	H	Kodi	Përshkrimi	Burimi
PK1	7515395.667	4692703.006	616.297	11	Monoment	PM
90374	7515359.360	4692531.510	905.350	2	Kunjë - shtyllë metalik	PM
90375	7515427.351	4692521.387	903.754	2	Kunjë - shtyllë metalik	PM
90376	7515418.492	4692554.630	902.838	2	Kunjë - shtyllë metalik	PM
90761	7515378.360	4692567.113	902.711	2	Kunjë - shtyllë metalik	PM
90762	7515384.555	4692567.943	901.521	2	Kunjë - shtyllë metalik	PM
90763	7515388.343	4692552.745	879.715	2	Kunjë - shtyllë metalik	PM
90765	7515336.041	4692534.979	880.462	2	Kunjë - shtyllë metalik	PM
90766	7515312.360	4692538.500	881.013	2	Kunjë - shtyllë metalik	PM
90767	7515289.010	4692541.980	884.904	2	Kunjë - shtyllë metalik	PM
90768	7515265.830	4692545.430	901.634	2	Kunjë - shtyllë metalik	PM
90769	7515258.706	4692546.490	899.754	2	Kunjë - shtyllë metalik	PM
90770	7515250.365	4692581.535	896.862	2	Kunjë - shtyllë metalik	PM
90771	7515357.727	4692565.867	890.697	2	Kunjë - shtyllë metalik	PM
92106	7515378.620	4692565.820	892.314	2	Kunjë - shtyllë metalik	PM
1	7515310.072	4692572.822	615.967	2	Kunjë - shtyllë metalik	PM
2	7515305.216	4692539.544	615.888	2	Kunjë - shtyllë metalik	PM
10	7515350.833	4692566.873	615.598	2	Kunjë - shtyllë metalik	PM
11	7515352.601	4692532.516	615.472	2	Kunjë - shtyllë metalik	PM

Matja e pikave në dy seri							
Seria	Nr. Pikës	Y	X	H	ΔY	ΔX	ΔP
I	1	7515310.06	4692572.81	615.97	-0.0050	-0.0270	0.0275
II	1	7515310.07	4692572.84	616.06			
I	2	7515305.23	4692539.541	615.89	0.0160	0.0050	0.0168
II	2	7515305.214	4692539.536	615.92			

Koordinatat përfundimtare			
Nr	Y	X	H
736149	7515310.066	4692572.822	616.013
736179	7515305.222	4692539.539	615.905

Gjeodeti / Kompania gjeodete e licencuar:	LIRIDON SEJDIU	Nënshkrimi dhe vula:
Numri i licencës	140	



Republika e Kosovës
Republika Kosova-Republic of Kosovo
Qeveria e Kosovës- Vlada Kosova- Government of Kosovo

Ministria e Infrastrukturës dhe Ambientit/ Ministrastvo Infrastrukture i Sredine/ Ministry of Infrastructure and Environment

AGJENCIA KADASTRALE E KOSOVËS/KOSOVSKA KATASTARSKA AGENCIJA/ KOSOVO CADASTRAL AGENCY

RAPORTI TEKNIK

Gjeodeti / Kompania gjeodete e licencuar: Liridon Sejdiu	Numri i licencës: 140
Komuna: Ferizaj	Zona Kadastrale: Bibaj
Numri i njësisë kadastrale: 00598-28	Lloji i lëndës: Ndarje e parcelës

Bazuar në kërkesën e palës **Mexhid (Hafiz) Behluli** me numër personal **1011785421** të parashtruar me datën **21/08/2020**, është bërë kërkesa përmarrjen e produkteve kadastrale në Zyrën Kadastrale Komunale **Ferizaj** me datë **21/08/2020**. Pas analizimit të dhënave me datë **22/08/2020** janë realizuar matjet në terren, përmarrje (ndarjen/bashkimin) e parcelave bazuar në (gjendjen faktike/sipërfaqe të barazuara).

Matjet në terren janë realizuar me instrument (GPS Leica 1230), ku fillimisht është bërë matja e pikës kontrolluese **PK1(Pikë rrredit III)** pastaj matjet janë realizuar bazuar në kornizën AKK nr.: 2020/01

Matje të dyfishta kontrolluese janë realizuar në pikat numër 1,2

Sfidat gjatë realizimit të

matjeve: _____

Matje të dyfishta kontrolluese janë realizuar në pikat numër 1,2.

Raporti në formë tabelare:

Parcela para ndarjes/bashkimit	Sipërfaqja (m ²)	Korigjimi i sipërfaqe (po/jo)	Parcela pas ndarjes/bashkimit	Sipërfaqja (m ²)
00598-28	5616	jo	00598-33	1800
			00598-34	1500
			00598-35	2316

Nënshkrimi dhe vula e gjodetit: _____

Data: 25/08/2020